


SITE STATISTICS

EXISTING LOT AREA:	6,000 ft ² (557 m ²)
PROPOSED BUILDING AREA:	1,741 ft ² (162 m ²)
LOT COVERAGE (30% MAX):	29.0%

PROPOSED SIDE YARD AREA (NORTH):	682 ft ² (63 m ²)
SIDE YARD SOFT LANDSCAPING (75% MIN.):	619 ft ² (58 m ²) [90%]
PROPOSED REAR YARD AREA:	1125 ft ² (105 m ²)
REAR YARD SOFT LANDSCAPING (50% MIN.):	751 ft ² (70 m ²) [67%]

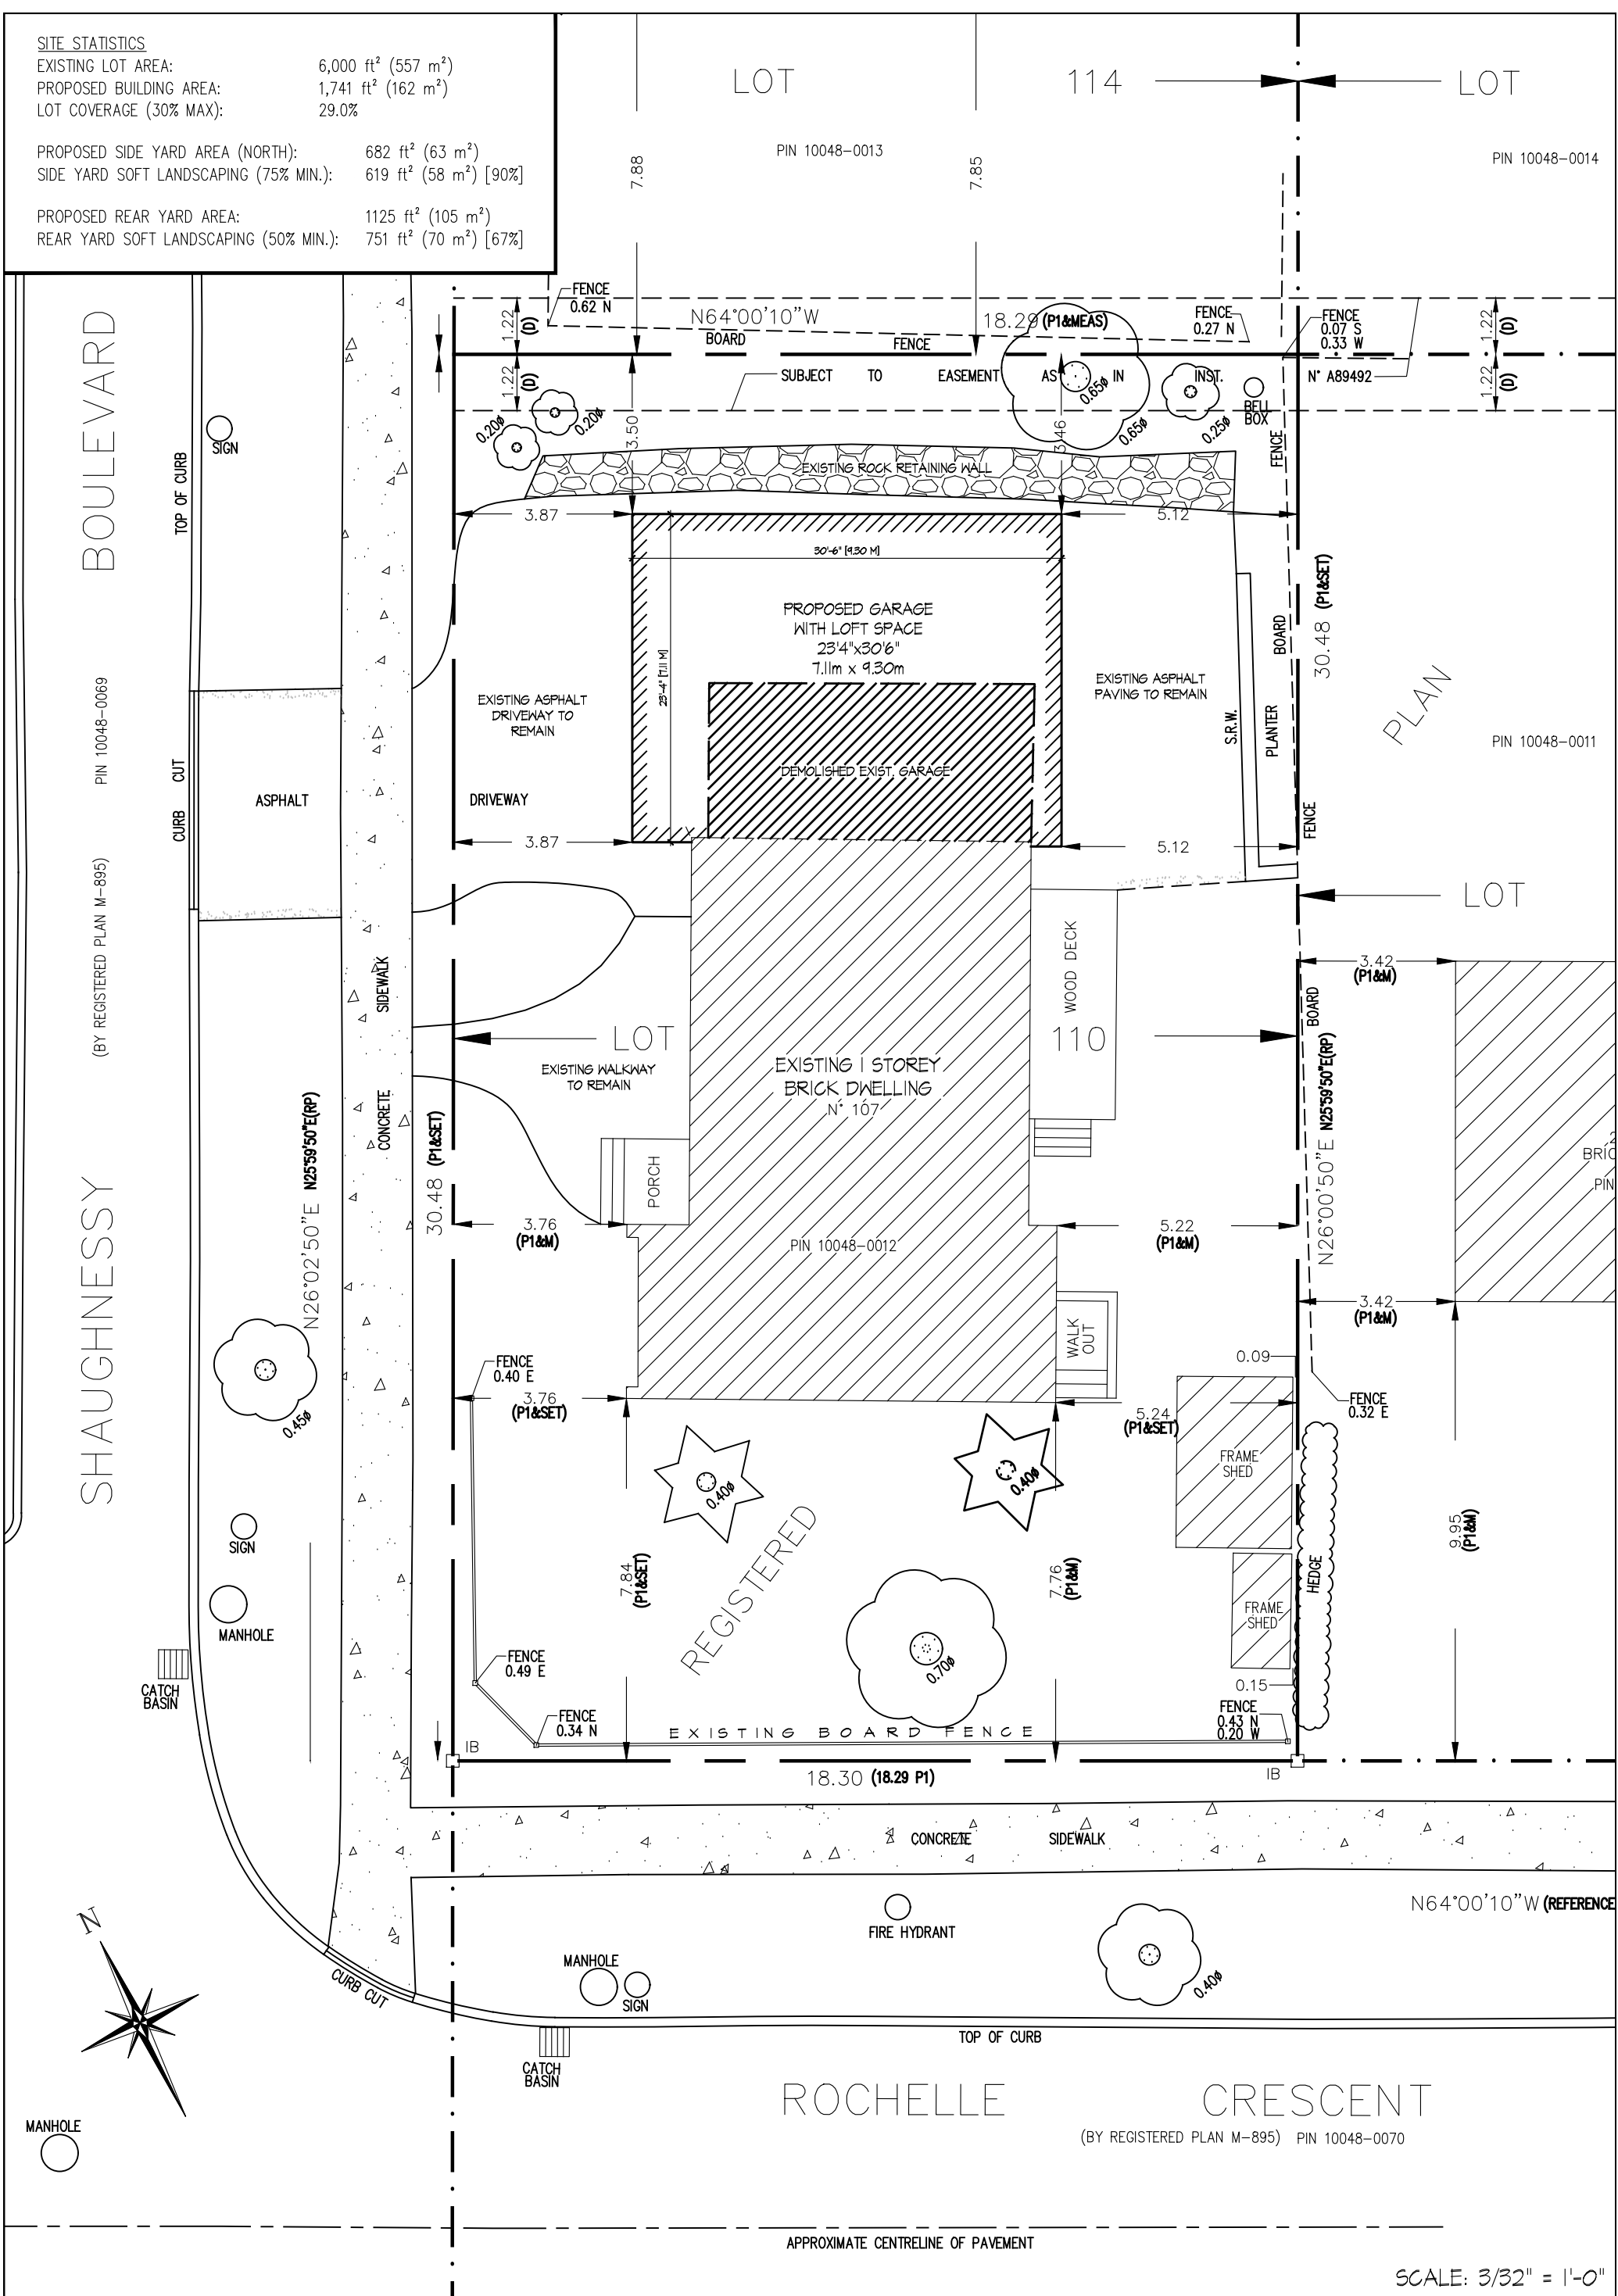

No.	DESCRIPTION	DATE	INT.	PROJECT: PROPOSED GARAGE W/ LOFT DEMO. EXISTING GARAGE ADDRESS: 107 SHAUGHNESSY BLVD. TORONTO, ONT. M2J 1J6	DRAWING: PROPOSED SITE PLAN
1	REVISED & RESUBMITTED FOR ZAP REVIEW	2023/05/30	WT		PAGE: SP-1
2					
3					
4					
5					
6					